10

Voorgevel

10

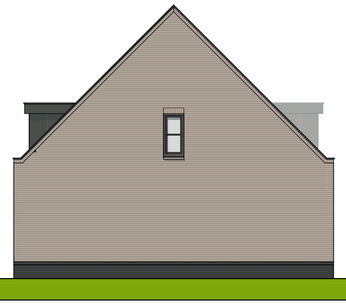

Rechtergevel 10

Achtergevel

Doorsnede 10-10

## RENVOOI ELEKTRA

- centraaldoos
- bedrade aansluiting in doos
  - utp : data aansluiting
  - th : thermostaat
  - rr : naregeling vloerverwarming
  - wtw : bediening wtw (zie BENG)
  - Co2 : Co2 sensor wtw (zie BENG)
- bel drukker (op intercom)
- enkele wandcontactdoos
- dubbele wandcontactdoos (horizontaal)
- dubbele wandcontactdoos (opbouw)
- enkele wandcontactdoos (waterdicht)
- lichtpunt (excl. armatuur)
- wandlichtpunt (excl. armatuur)
- LED inbouwspot
- schakelaar
- schakelaar + wandcontactdoos (horizontaal)
- wisselschakelaar
- rookmelder
- vloerverwarming verdeler
- voorziening excl. radiator elektrisch
- buitenkraan met afvoerputje
- omvormer — omvormer PV-panelen

De maatvoering op tekening is indicatief en kan afwijken, maten in millimeters. Indien deze maatvoering tussen wanden is aangegeven, is daarbij geen rekening gehouden met enige wandafwerking.
De netto bruikbare maten bij oplevering kunnen een aantal centimeters van de genoemde bruto maten afwijken.
Aan deze maatvoering kunnen geen rechte worden ontleend.

De opstelling van de keuken en badkamer incl. aansluitingen volgens de nul-tekening van leveranciers.

De op tekening aangegeven elektrapunten/aansluitpunten/ radiatoren zijn indicatief.
De exacte plaats wordt nader bepaald door de installateur(s) / keukenleverancier.
Elektrapunten in woningscheidende wanden niet ruggelings maar 300mm. laten
verspringen, ook als op tekening anders is aangegeven.
Het is mogelijk dat niet alle symbolen in het renvooi van toepaassing zijn op uw woning.

Binnenkozijnen stalen nastel kozijnen voorzien van opdekdeuren.

0 5 10 m

SCHAAL GEVELS

0 5

SCHAAL PLATTEGRONDEN

## RENVOOI KEUKEN

2x tweevoudige w.c.d. voor algemeen gebruik 1100+
1x enkelvoudige w.c.d. voor wasemkap met verlichting
1x enkelvoudige w.c.d. voor koelkast/vriezer
1x enkelvoudige w.c.d. voor vaatwasser
1x enkelvoudige w.c.d. voor oven / magnetron
1x loze leding tbv boiler / Quooker
1x 3-fase kookgroep (perilex aansluiting)

Exacte plaats (x-y-z richting) volgens
nadere opgave keuken leverancier

## RENVOOI BADKAMER / TOILET

-water +riool aansluitingen
X-Y richting volgens nadere opgave badkamer leverancier
Z-richting in basis 100mm bk peil afgedopt.

-hoogte smeervloer tot bovenkant vloerverwarming
-douchehoek wordt gespaard (smeervloer)
indeling conform badkamer tekening
(douchehoek wordt niet voorzien van vloerverwarming )

## MONTAGE HOOGTES

| | |
|---|---|
| - Schakelaars | :1050mm + P |
| - Wandcontactdozen, data (utp) | : 300mm + P |
| - Wandlichtpunten buiten | :2200mm + P |
| - Wandlichtpunten binnen | :2200mm + P |
| - Thermostaat (th) / ruimteregeling (nar) | :1500mm + P |

## RENVOOI INSTALLATIES

* positie installaties, aantal leidingschachten en ventilatiepunten, riolering zijn indicatief weergegeven
* specificatie installaties conform BENG-berekening

- opstelplaats warmteterugwinunit (WTW)
- warmtepomp met interne boiler
- opstelplaats wasmachine
- opstelplaats wasdroger
- mechanische afvoer
- mechanische toevoer
- ruimte vzv. vloerverwarming

Na ondertekening zijn het ontwerp, en gemaakte afspraken bevestigd en vrijgegeven voor inschrijving naar de aannemer. Op basis van deze stukken vindt de calculatie plaats.

*Naam:*

*Datum:*

*Handtekening:*

Na ondertekening zijn in deze fase geen wijzigingen meer mogelijk op het ontwerp. Eventuele verdere uitwerking of afstemming vanuit adviseurs kan, indien van toepassing, uitsluitend als meerwerk via de aannemer worden verwerkt. Eventuele opties uit de optielijst verlopen via de kopersbegeleider van de aannemer als meerwerk.
**Het ondertekende exemplaar ontvangen wij graag uiterlijk 28 oktober.**

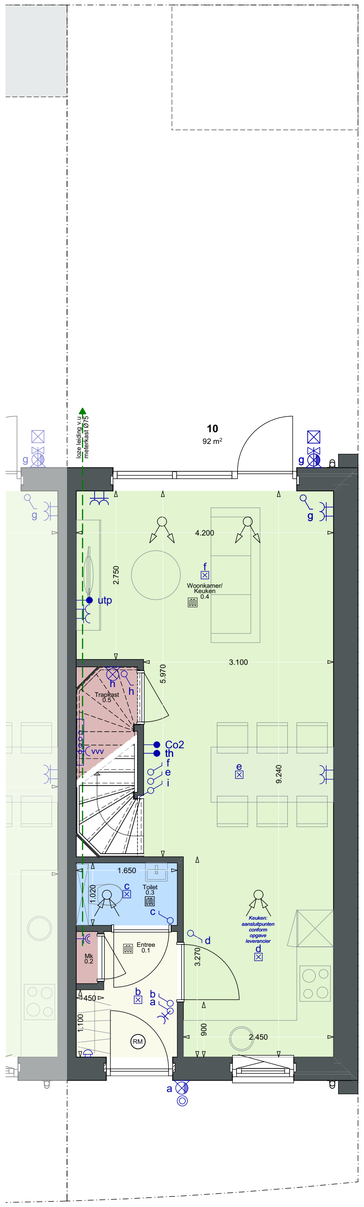


Begane grond

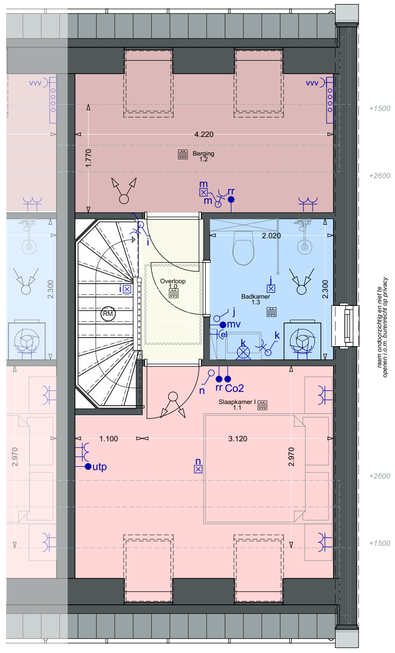


1e verdieping

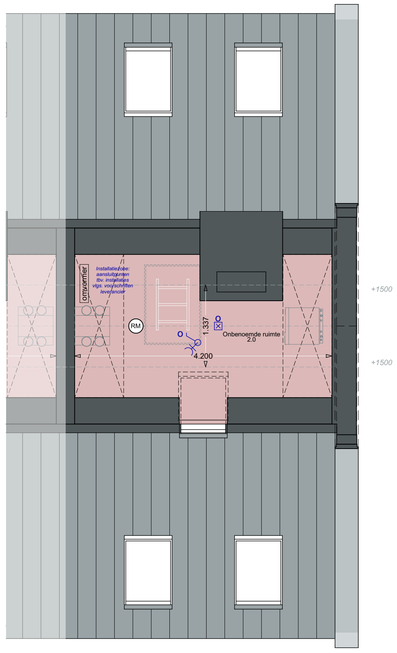


Zolder

Gemeente: Heeze
Sectie : C
Nummer : 4951
Schaal : 1:2000

Situatie


**keeris** architecten
Dijk 14 5521 AX Eersel T: 0497-514480


CPO Heeze, Bulders

Kavel 10

| | | | | | |
|---|---|---|---|---|---|
| tekenaar: | ir. WK / BE | werknummer: | C24001 | tekening: | VK-10 |
| schaal: | 1:100 | datum: | 29-10-2025 | | |


www.keerisarchitecten.nl info@keerisarchitecten.nl



*maten in millimeters tenzij anders aangegeven - alle maten in het werk te controleren - gegevens constructeur te allen tijde maatgevend*